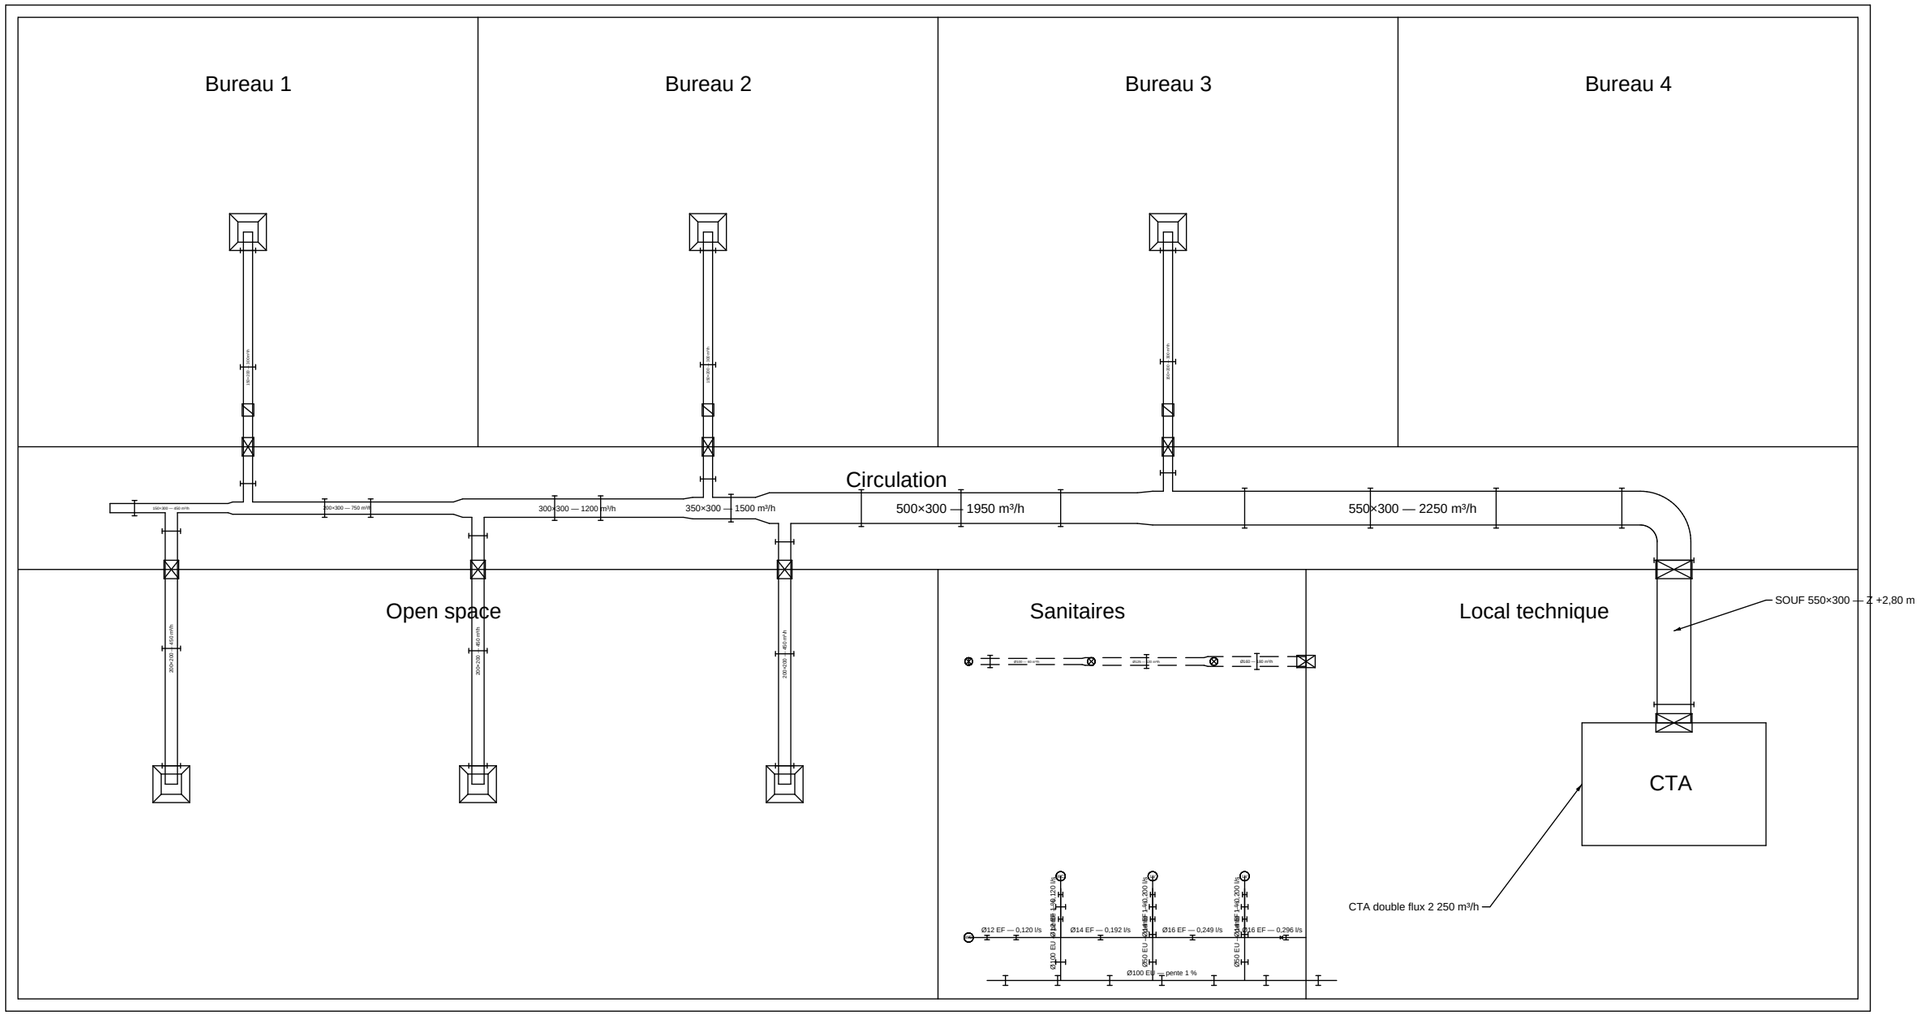


Démo MEP — plan CVC et plomberie — 1:100 (dessin créé dans CAD Viewer)